


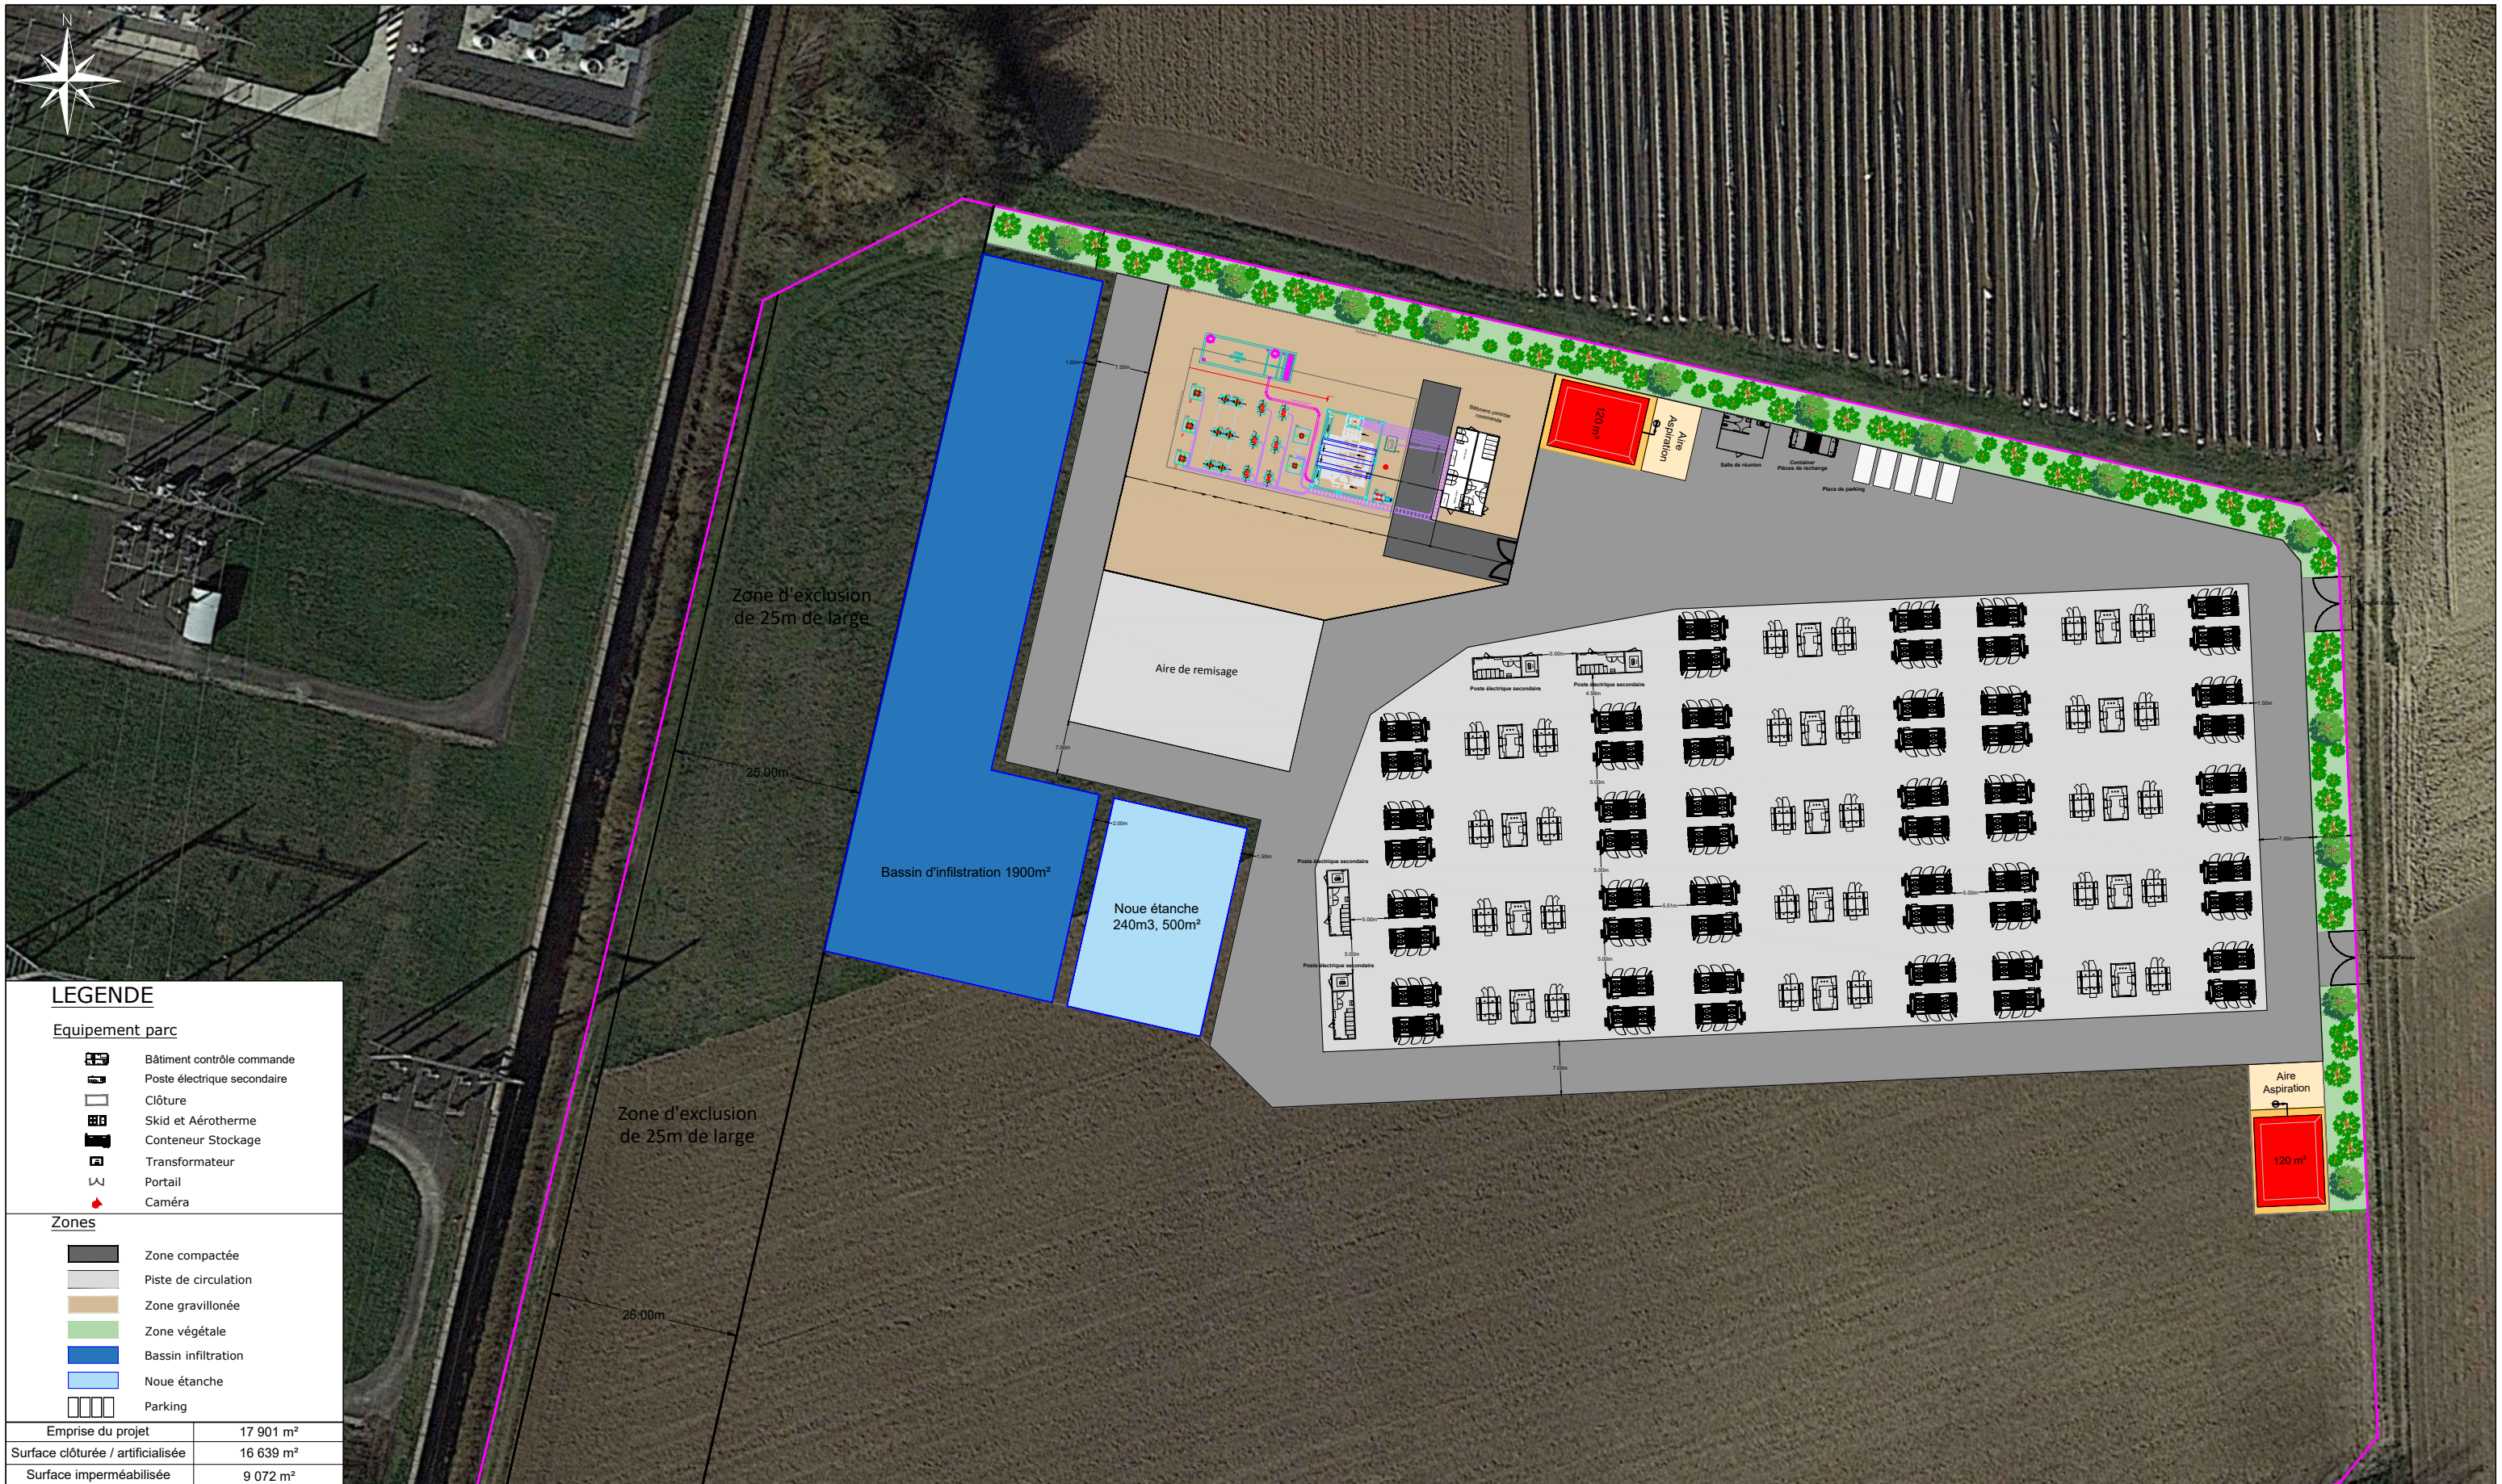

Plan d'Implantation

Projet:

Marlenheim

Adresse Projet:

67520 Marlenheim

Puissance Projet :

Puissance = 110 MW // Energie = 220 MWh

Coordonnées GPS:

48.611602, 7.529392

Surface clôturée

Référence Document:

16 639 m²

N° Projet

—

Echelle:

1/800

APS

APS APD EXE DOE

Format:

A3

Page:

1/1

REVISIONS

Indice	Date	Dessiné	Vérifié	Approuvé	Description
A	19/07/2023	DC	BF	BF	Création
B	24/11/2023	PS			Modification, suppression des noues étanches et ajout du tableau
C	17/09/2024	DC	BF	BF	Maj. du plan
D	25/09/2024	DC	BF	BF	Maj. du plan

AMARENCO Construction, Château de Touny Les Roses - 32 Chemin de Touny 81150 LAGRAVE - Tel:05 63 34 20 42